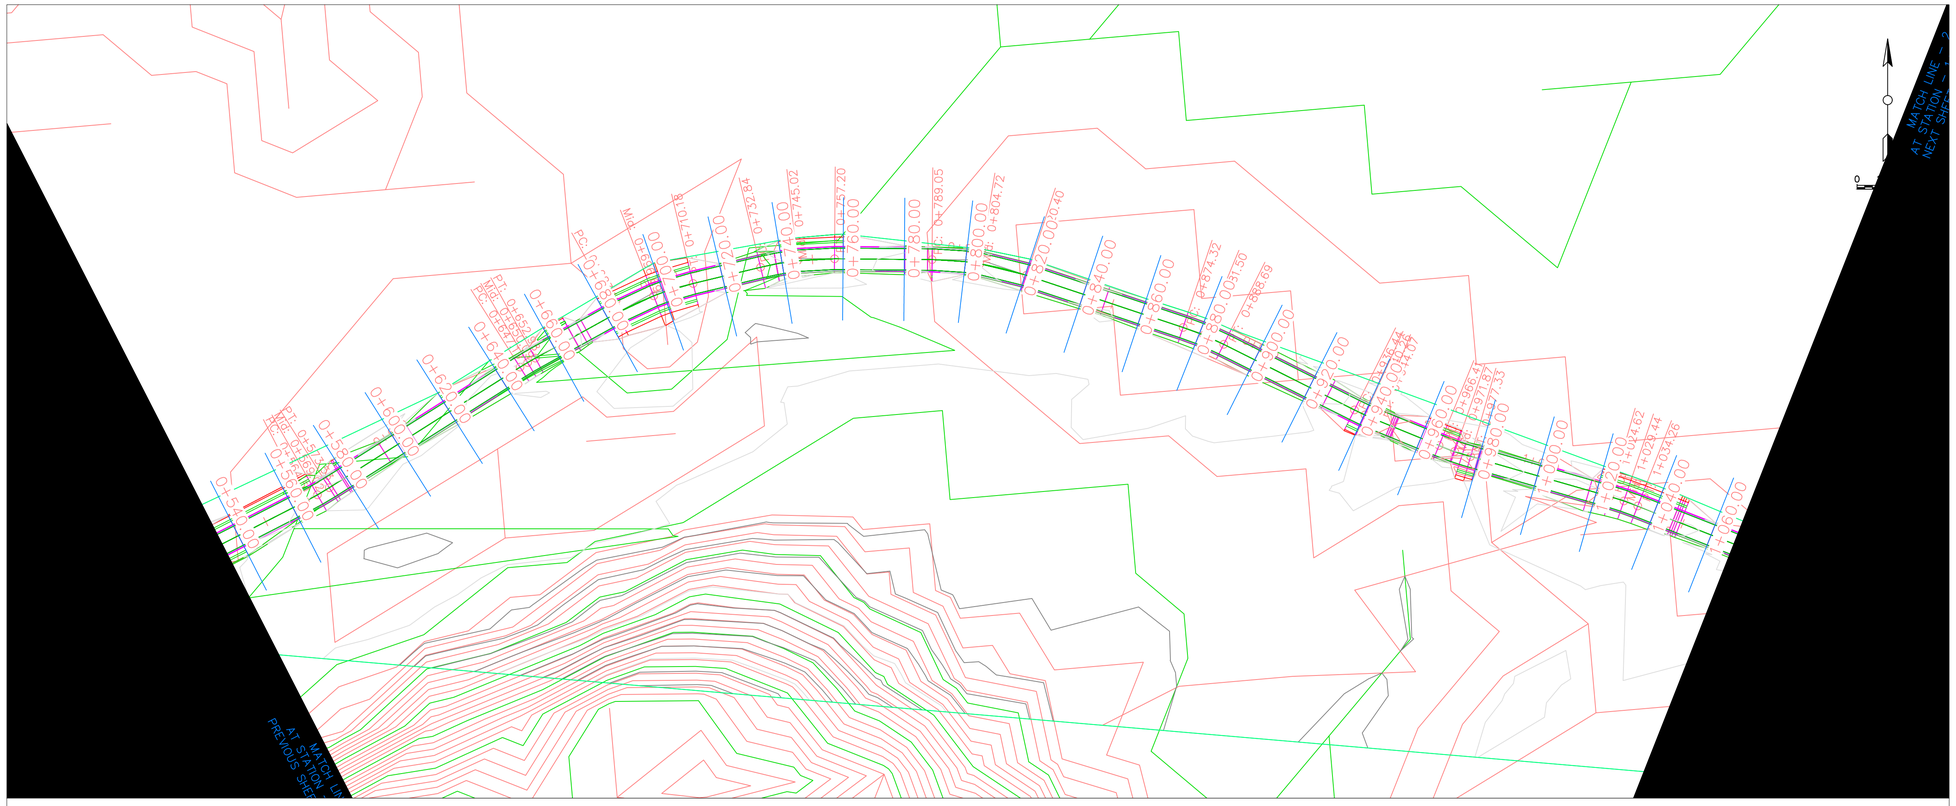

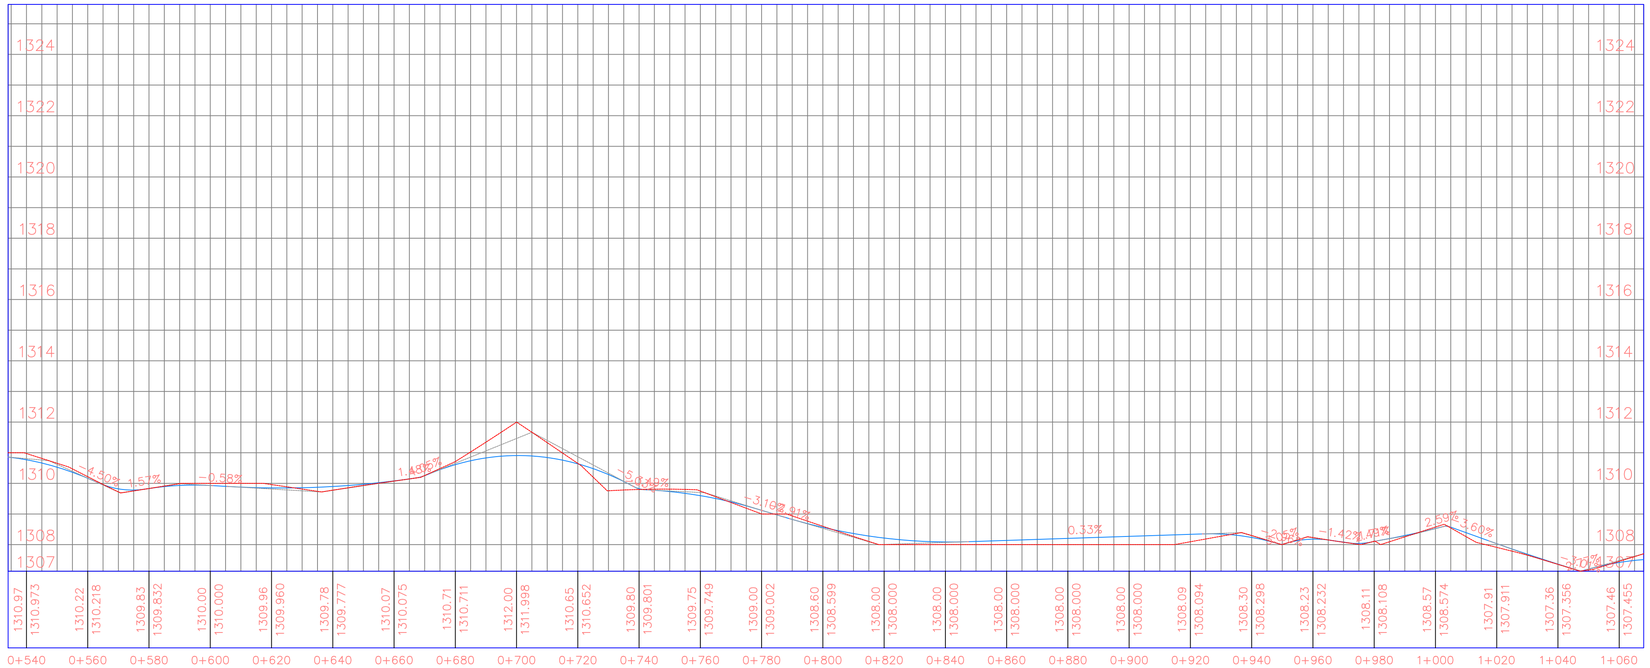

General Notes

No.	Revision/Issue	Date

Firm Name and Address

Drawn By: Bikrant Pandey

Project Name and Address

Road Design

Project	Sheet
Profile 2	2
Date: 21.04.2026	
Scale: 1:1000	

19.03.2007 Road01 Design (1).dwg